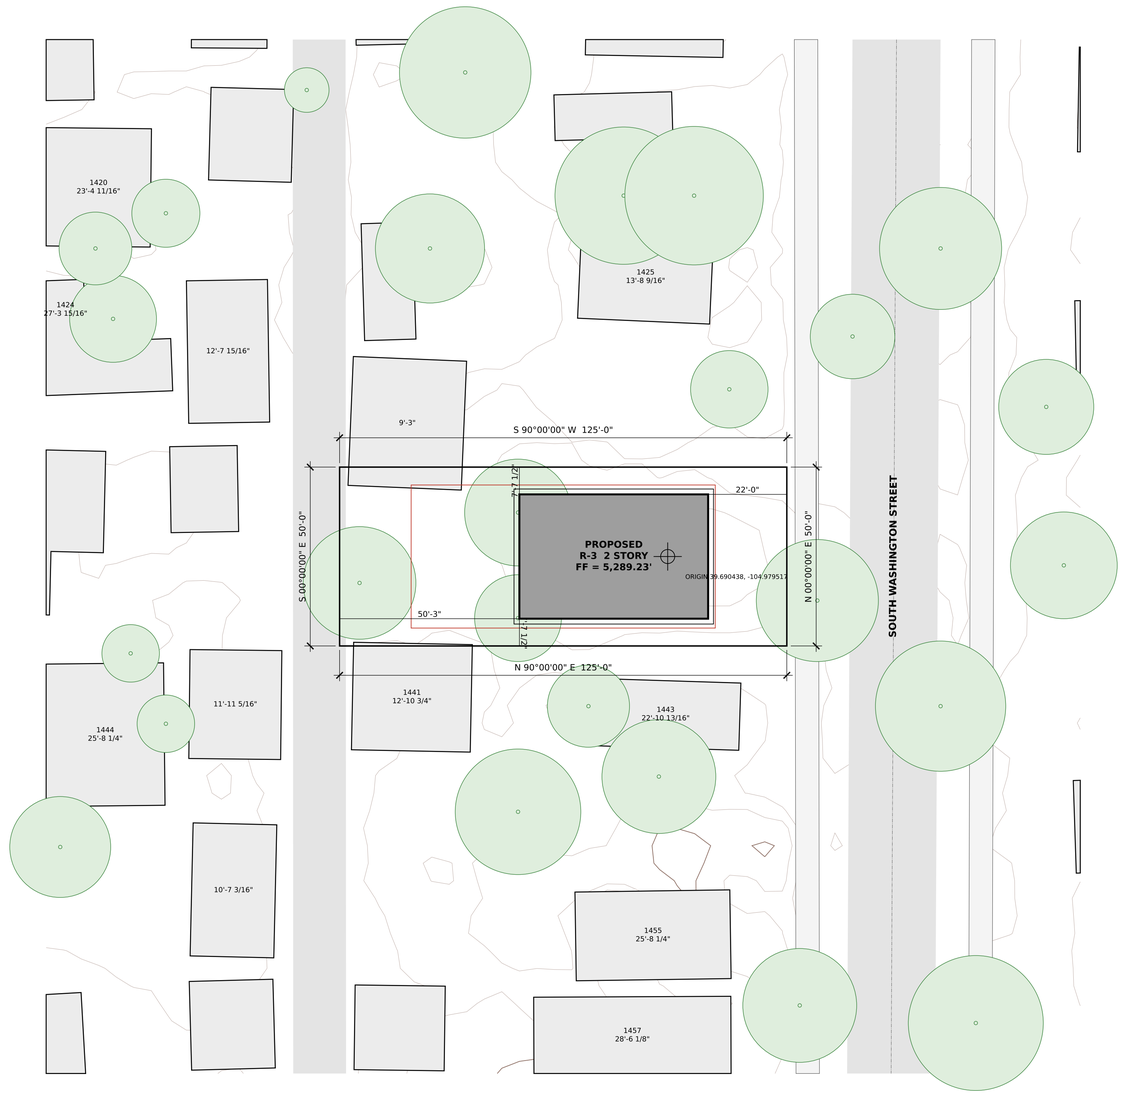


SITE DATA

Zoning district	U-SU-C (assumed)
Lot area	6,250 SF
Building footprint	1,833 SF
Lot coverage	29.3%
Gross floor area	3,666 SF
FAR	0.59
Occupancy / Type	R-3 / V-B
Code profile	IRC-2021
Setback front	20'-0"
Setback side	5'-0"
Setback rear	20'-0"
Max height	30'-0"
Max lot coverage	0.375

COORDINATION

Checks	0 fail / 3 warn
WARN	parcel boundary source
WARN	existing building on footprint (14
WARN	existing building on footprint (So

DATA SOURCES

© OpenStreetMap contributors (ODbL)
USGS 3DEP LiDAR CO_DRCOG_2_2020 (public doma
* = height estimated (untagged)

ARCHKIT STUDIO

PROJECT
Platt Park Infill Residence

ADDRESS
1435 S Washington St, Denver, CO 80210

CLIENT
Example Client

PROJECT NO.
2026-014

ISSUE
SCHEMATIC DESIGN

DATE
2026-11-09


GENERAL NOTES

1. Lot lines approximate (standard Denver lot); obtain boundary survey.
2. Existing structure at 1435 S Washington St to be demolished.
3. PRELIMINARY — NOT FOR CONSTRUCTION.
4. Site context from public data; verify with boundary & topographic survey.
5. Code checks are preliminary; AHJ review governs.

1 C1.0 **ARCHITECTURAL SITE PLAN**
SCALE: 1" = 20'

0 8 16 24 32 FT

SITE PLAN
C1.0
archkit

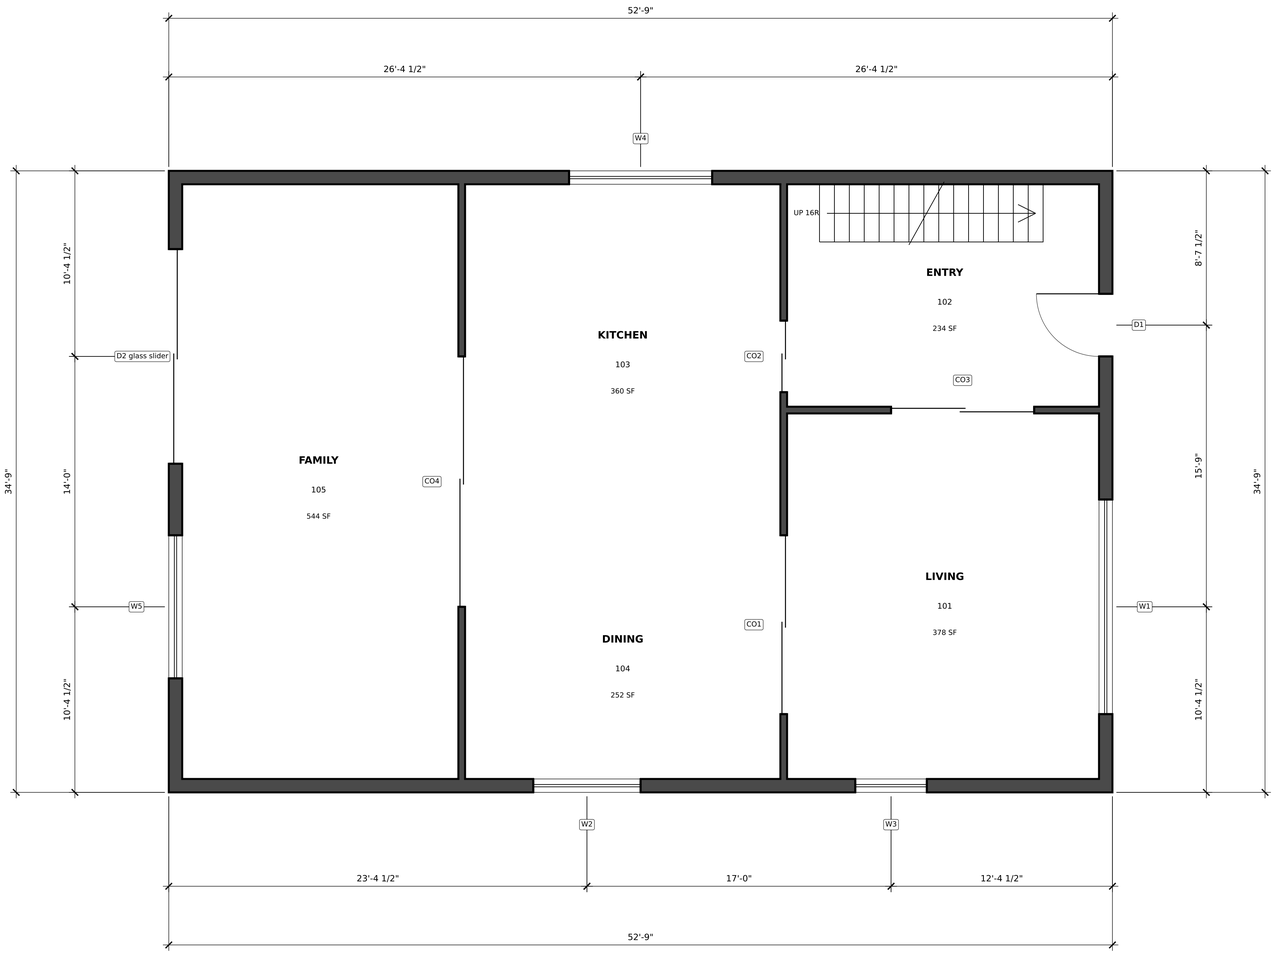

1 / A1.1 **LEVEL 1 FLOOR PLAN**

SCALE: 1/4" = 1'-0"

0 1.25 2.5 3.75 5 FT

TRUE NORTH

ARCHKIT STUDIO

PROJECT
Platt Park Infill Residence

ADDRESS
1435 S Washington St, Denver, CO 80210

CLIENT
Example Client

PROJECT NO.
2026-014

ISSUE
SCHEMATIC DESIGN

DATE
2026-11-09


GENERAL NOTES

1. Lot lines approximate (standard Denver lot); obtain boundary survey.
2. Existing structure at 1435 S Washington St to be demolished.
3. PRELIMINARY — NOT FOR CONSTRUCTION.
4. Site context from public data; verify with boundary & topographic survey.
5. Code checks are preliminary; AHJ review governs.

LEVEL 1 FLOOR PLAN

A1.1

archkit

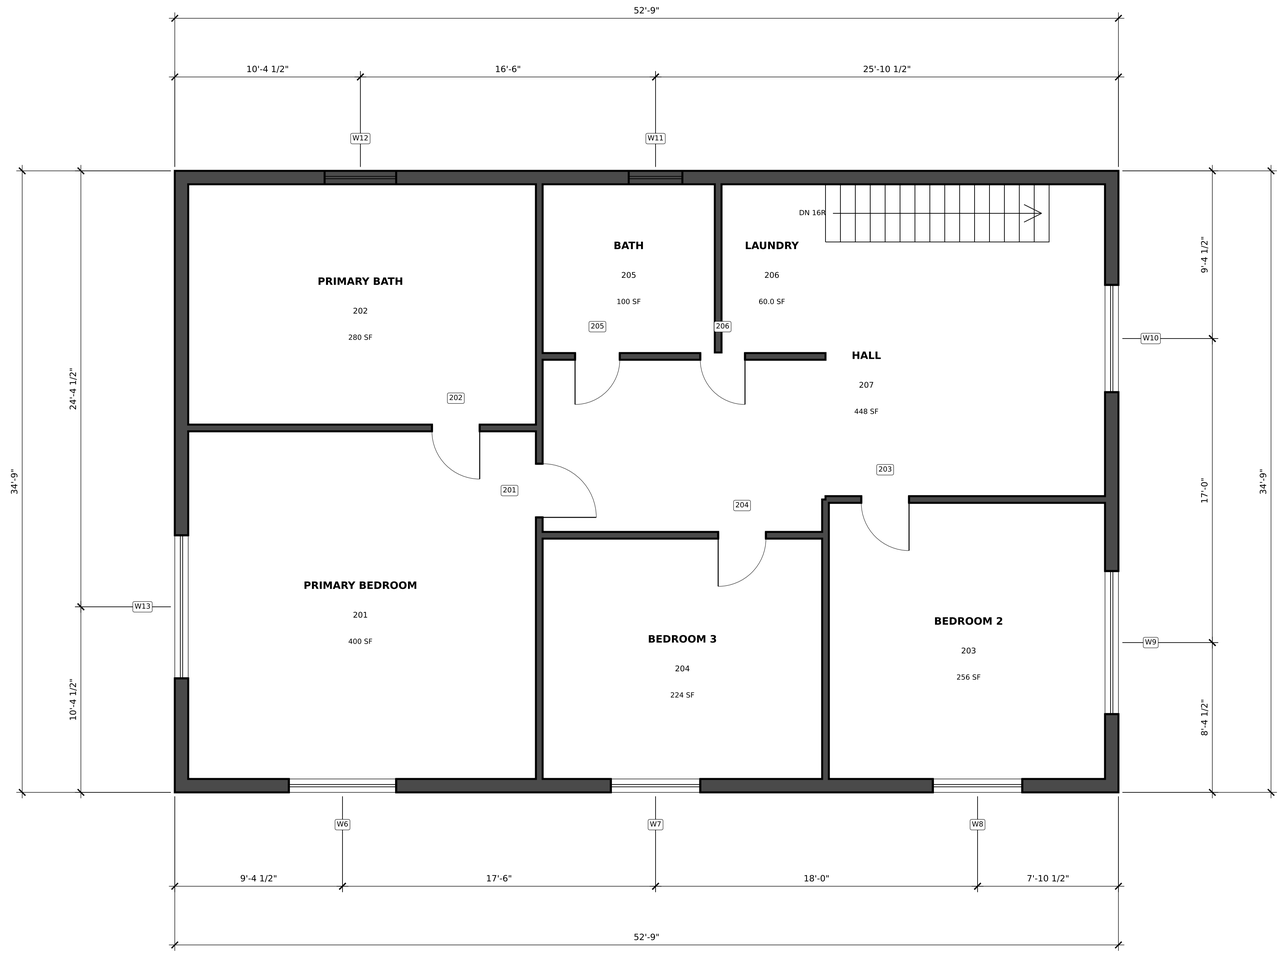

1 / A1.2 **LEVEL 2 FLOOR PLAN**

SCALE: 1/4" = 1'-0"

0 1.25 2.5 3.75 5 FT

N

TRUE NORTH

ARCHKIT STUDIO

PROJECT
Platt Park Infill Residence

ADDRESS
1435 S Washington St, Denver, CO 80210

CLIENT
Example Client

PROJECT NO.
2026-014

ISSUE
SCHEMATIC DESIGN

DATE
2026-11-09


GENERAL NOTES

1. Lot lines approximate (standard Denver lot); obtain boundary survey.
2. Existing structure at 1435 S Washington St to be demolished.
3. PRELIMINARY — NOT FOR CONSTRUCTION.
4. Site context from public data; verify with boundary & topographic survey.
5. Code checks are preliminary; AHJ review governs.

LEVEL 2 FLOOR PLAN


A1.2

archkit

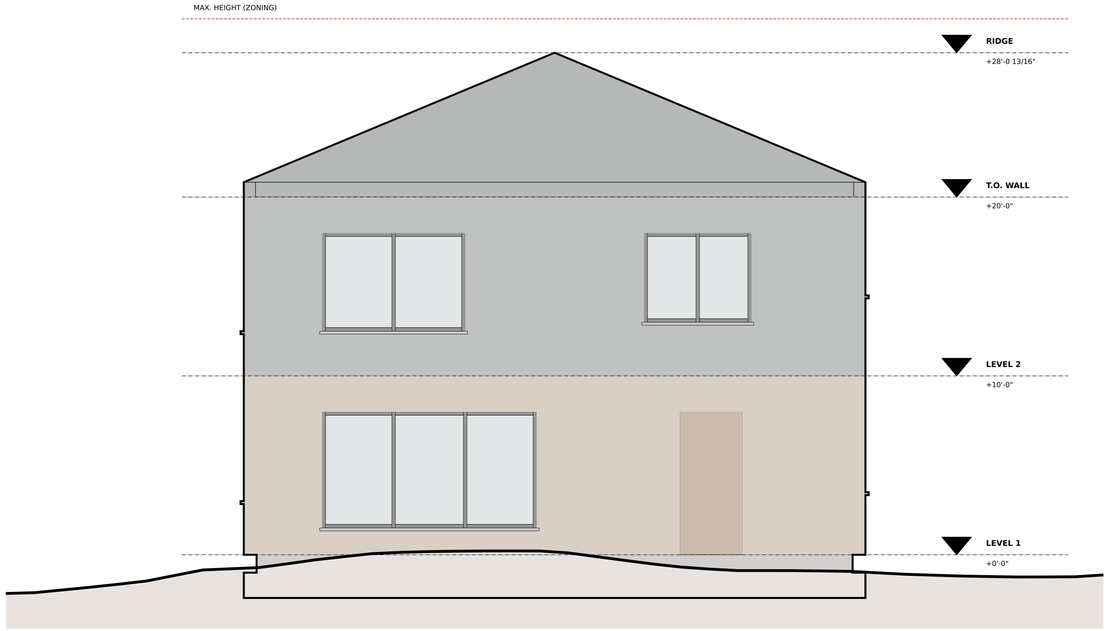

1 A2.0 **EAST ELEVATION**
SCALE: 1/4" = 1'-0"

0 1.25 2.5 3.75 5 FT

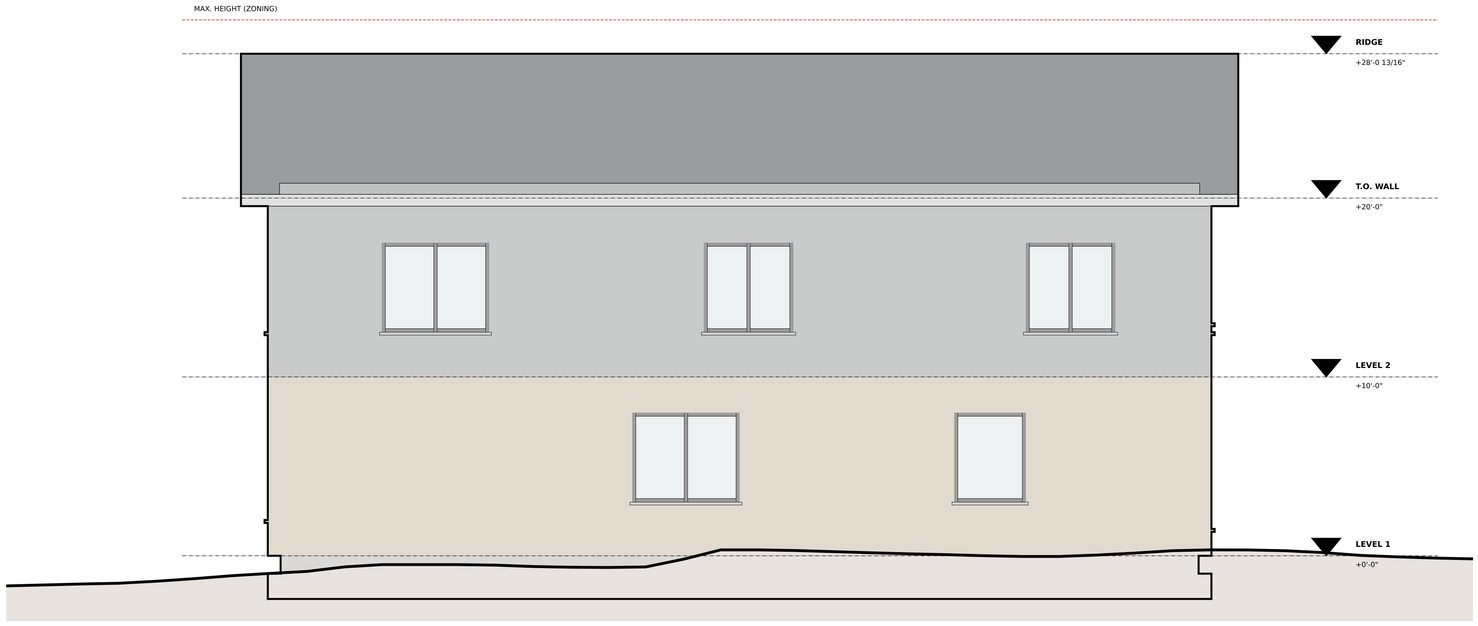

2 A2.0 **SOUTH ELEVATION**
SCALE: 1/4" = 1'-0"

0 1.25 2.5 3.75 5 FT

ARCHKIT STUDIO

PROJECT
Platt Park Infill Residence

ADDRESS
1435 S Washington St, Denver, CO 80210

CLIENT
Example Client

PROJECT NO.
2026-014

ISSUE
SCHEMATIC DESIGN

DATE
2026-11-09


GENERAL NOTES

1. Lot lines approximate (standard Denver lot); obtain boundary survey.
2. Existing structure at 1435 S Washington St to be demolished.
3. PRELIMINARY — NOT FOR CONSTRUCTION.
4. Site context from public data; verify with boundary & topographic survey.
5. Code checks are preliminary; AHJ review governs.

EXTERIOR ELEVATIONS

A2.0


archkit

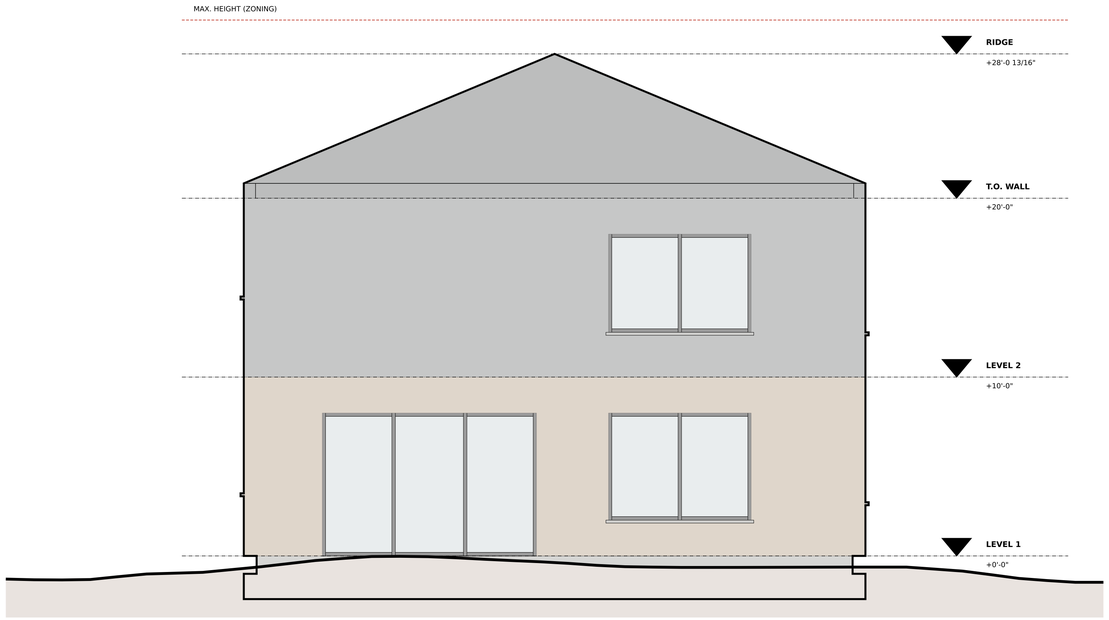

1 A2.1 **WEST ELEVATION**

SCALE: 1/4" = 1'-0"

0 1.25 2.5 3.75 5 FT

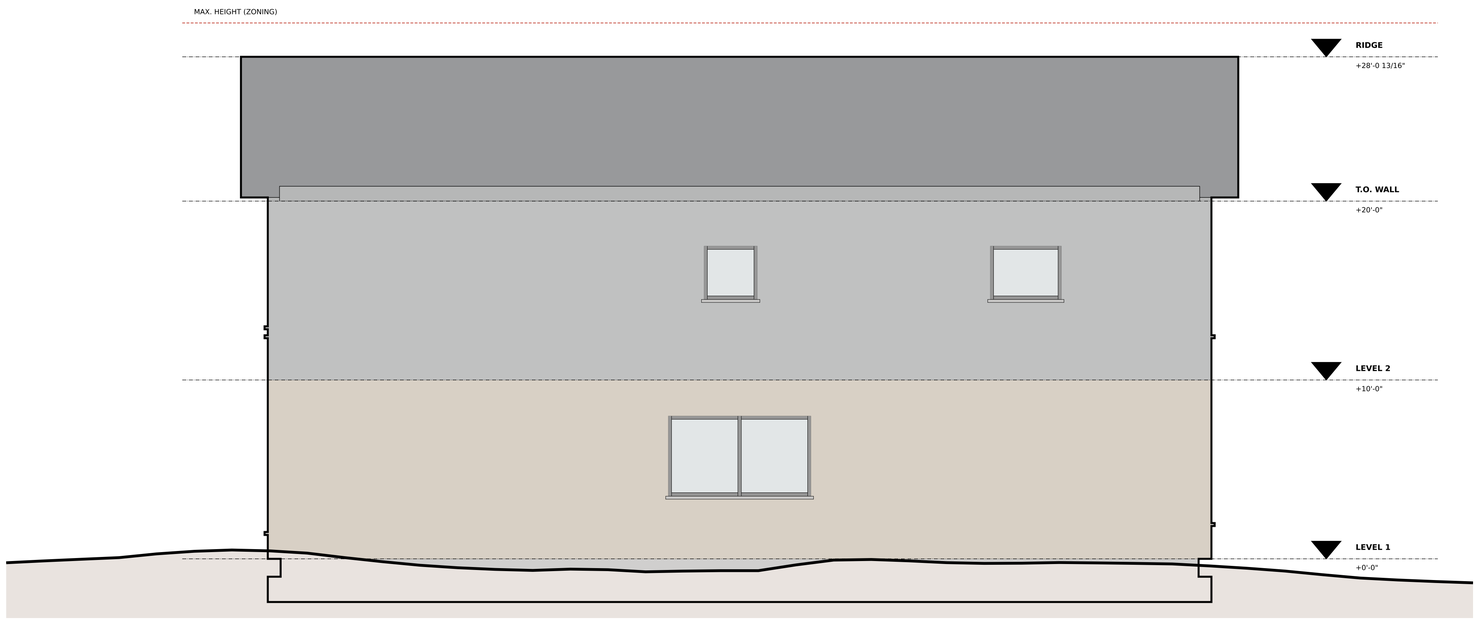

2 A2.1 **NORTH ELEVATION**

SCALE: 1/4" = 1'-0"

0 1.25 2.5 3.75 5 FT

ARCHKIT STUDIO

PROJECT
Platt Park Infill Residence

ADDRESS
1435 S Washington St, Denver, CO 80210

CLIENT
Example Client

PROJECT NO.
2026-014

ISSUE
SCHEMATIC DESIGN

DATE
2026-11-09

GENERAL NOTES

1. Lot lines approximate (standard Denver lot); obtain boundary survey.
2. Existing structure at 1435 S Washington St to be demolished.
3. PRELIMINARY — NOT FOR CONSTRUCTION.
4. Site context from public data; verify with boundary & topographic survey.
5. Code checks are preliminary; AHJ review governs.

EXTERIOR ELEVATIONS

A2.1


archkit



1 A3.0 **BUILDING SECTION A**

SCALE: 1/4" = 1'-0"

0 1.25 2.5 3.75 5 FT

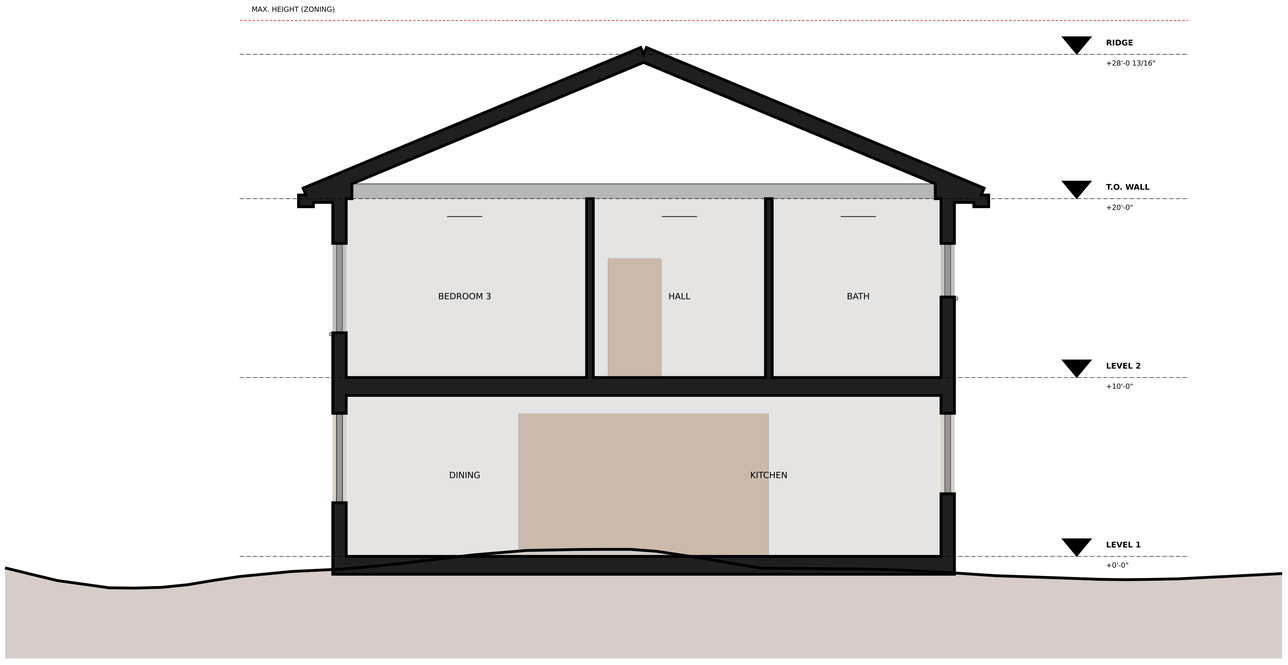

2 A3.0 **BUILDING SECTION B**

SCALE: 1/4" = 1'-0"

0 1.25 2.5 3.75 5 FT

ARCHKIT STUDIO

PROJECT
Platt Park Infill Residence

ADDRESS
1435 S Washington St, Denver, CO 80210

CLIENT
Example Client

PROJECT NO.
2026-014

ISSUE
SCHEMATIC DESIGN

DATE
2026-11-09

GENERAL NOTES

1. Lot lines approximate (standard Denver lot); obtain boundary survey.
2. Existing structure at 1435 S Washington St to be demolished.
3. PRELIMINARY — NOT FOR CONSTRUCTION.
4. Site context from public data; verify with boundary & topographic survey.
5. Code checks are preliminary; AHJ review governs.

BUILDING SECTIONS

A3.0

archkit